


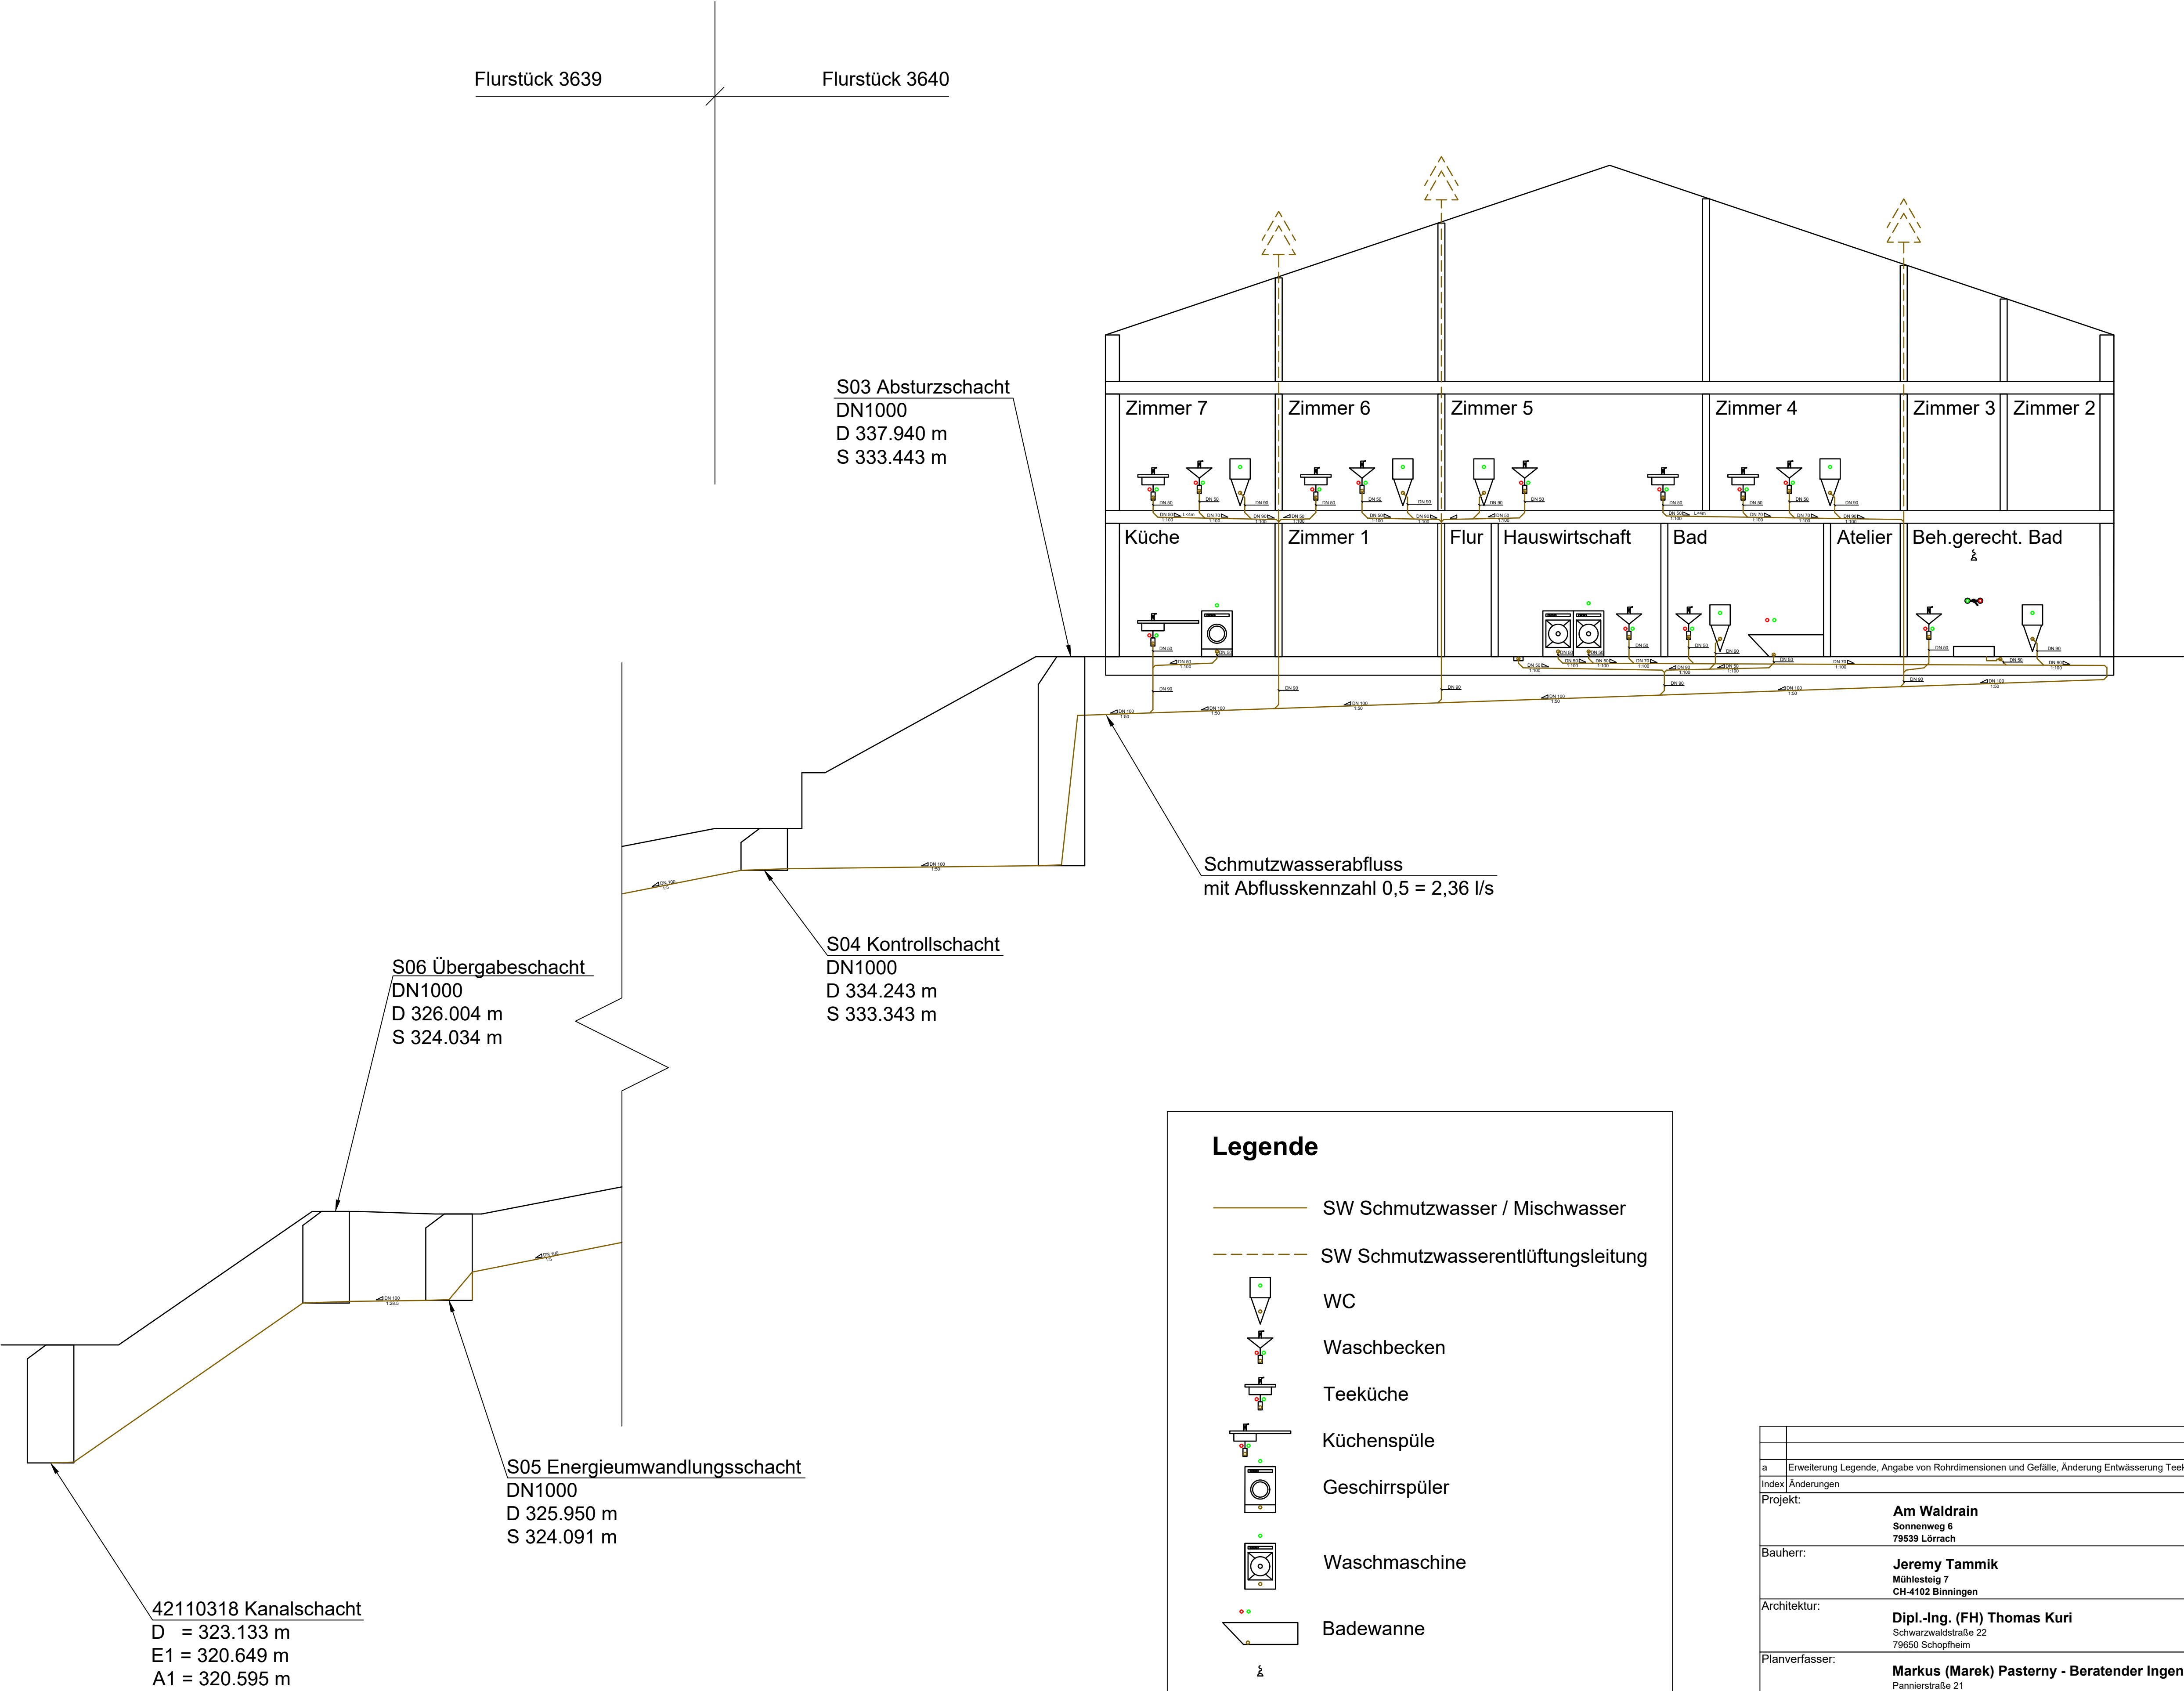

Legende

- SW Schmutzwasser / Mischwasser
- SW Schmutzwasserentlüftungsleitung
- WC
- Waschbecken
- Teeküche
- Küchenspüle
- Geschirrspüler
- Waschmaschine
- Badewanne
- Dusche

a	Erweiterung Legende, Angabe von Rohrdimensionen und Gefälle, Änderung Entwässerung Teeküche Zimmer 5	08.06.25	MPV
Index	Änderungen	Datum	Name
Projekt:			
Am Waldrain Sonnenweg 6 79539 Lörrach			
Bauherr:			
Jeremy Tammik Mühlesteg 7 CH-4102 Blinningen			
Architektur:			
Dipl.-Ing. (FH) Thomas Kuri Schwarzwaldstraße 22 79650 Schopfheim			
Planverfasser:			
Markus (Marek) Pasterny - Beratender Ingenieur Pannierstraße 21 12047 Berlin			
Projekt-Nr.:	Datum:	Maßstab:	Blattgröße:
25-007	02.06.2025	ohne	A1 (841x594) mm
Planbezeichnung:			Projektphase:
Strangschema Entwässerung			LP 4
Plan-Nr.: 007-4-SSE-551-----a			