


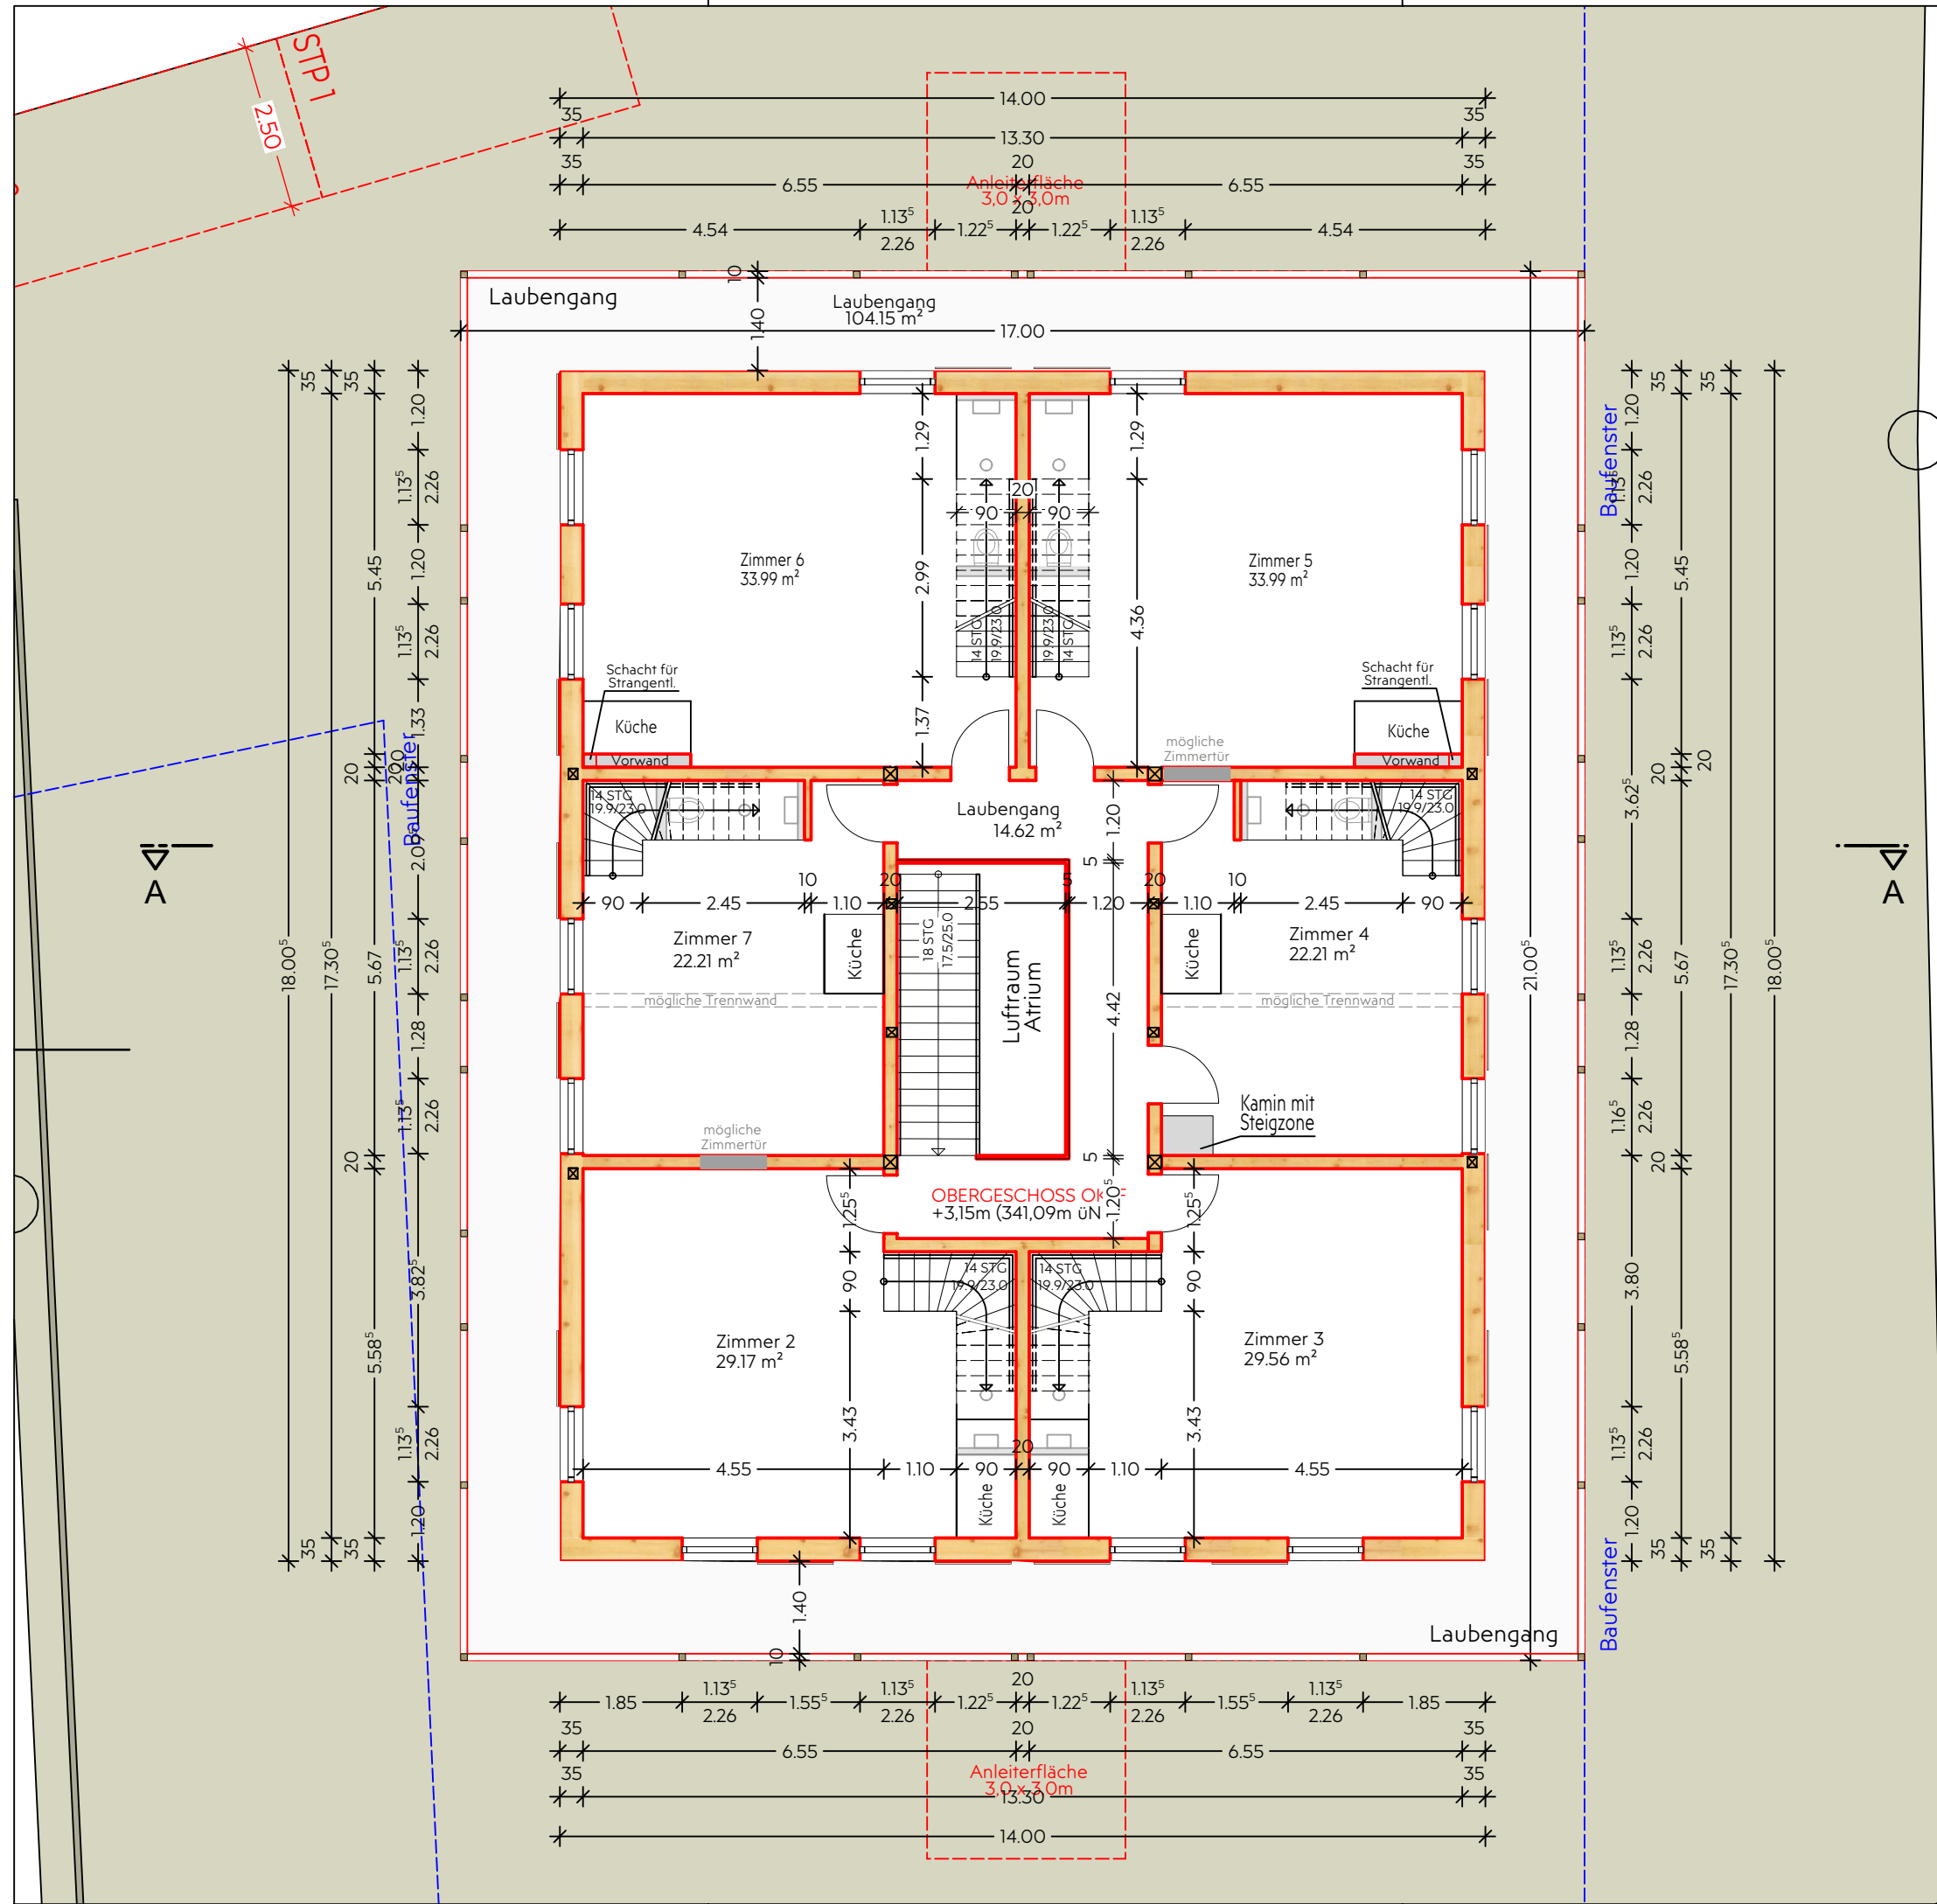

STATUS	BAUANTRAG <i>VORABZUG</i>		
PROJEKT	Neubau eines Wohnhauses mit gemeinschaftlich nutzbaren Wohneinheiten Sonnenweg 6 79539 Lörrach		
BAUHERR	Jeremy Tammik Mühlesteig 7 CH-4102 Binningen		
ARCHITEKT	KURIARCHITEKTEN BDA Belchenstraße 80 79650 Schopfheim +49 7622 684 36 75 info@kuriarchitekten.de kuriarchitekten.de		
PLAN	Grundriss - Obergeschoss A3		
DATUM	18.11.2024	1:100	LK
VERFASSER	Unterschrift Bauherr	Unterschrift Architekt	

