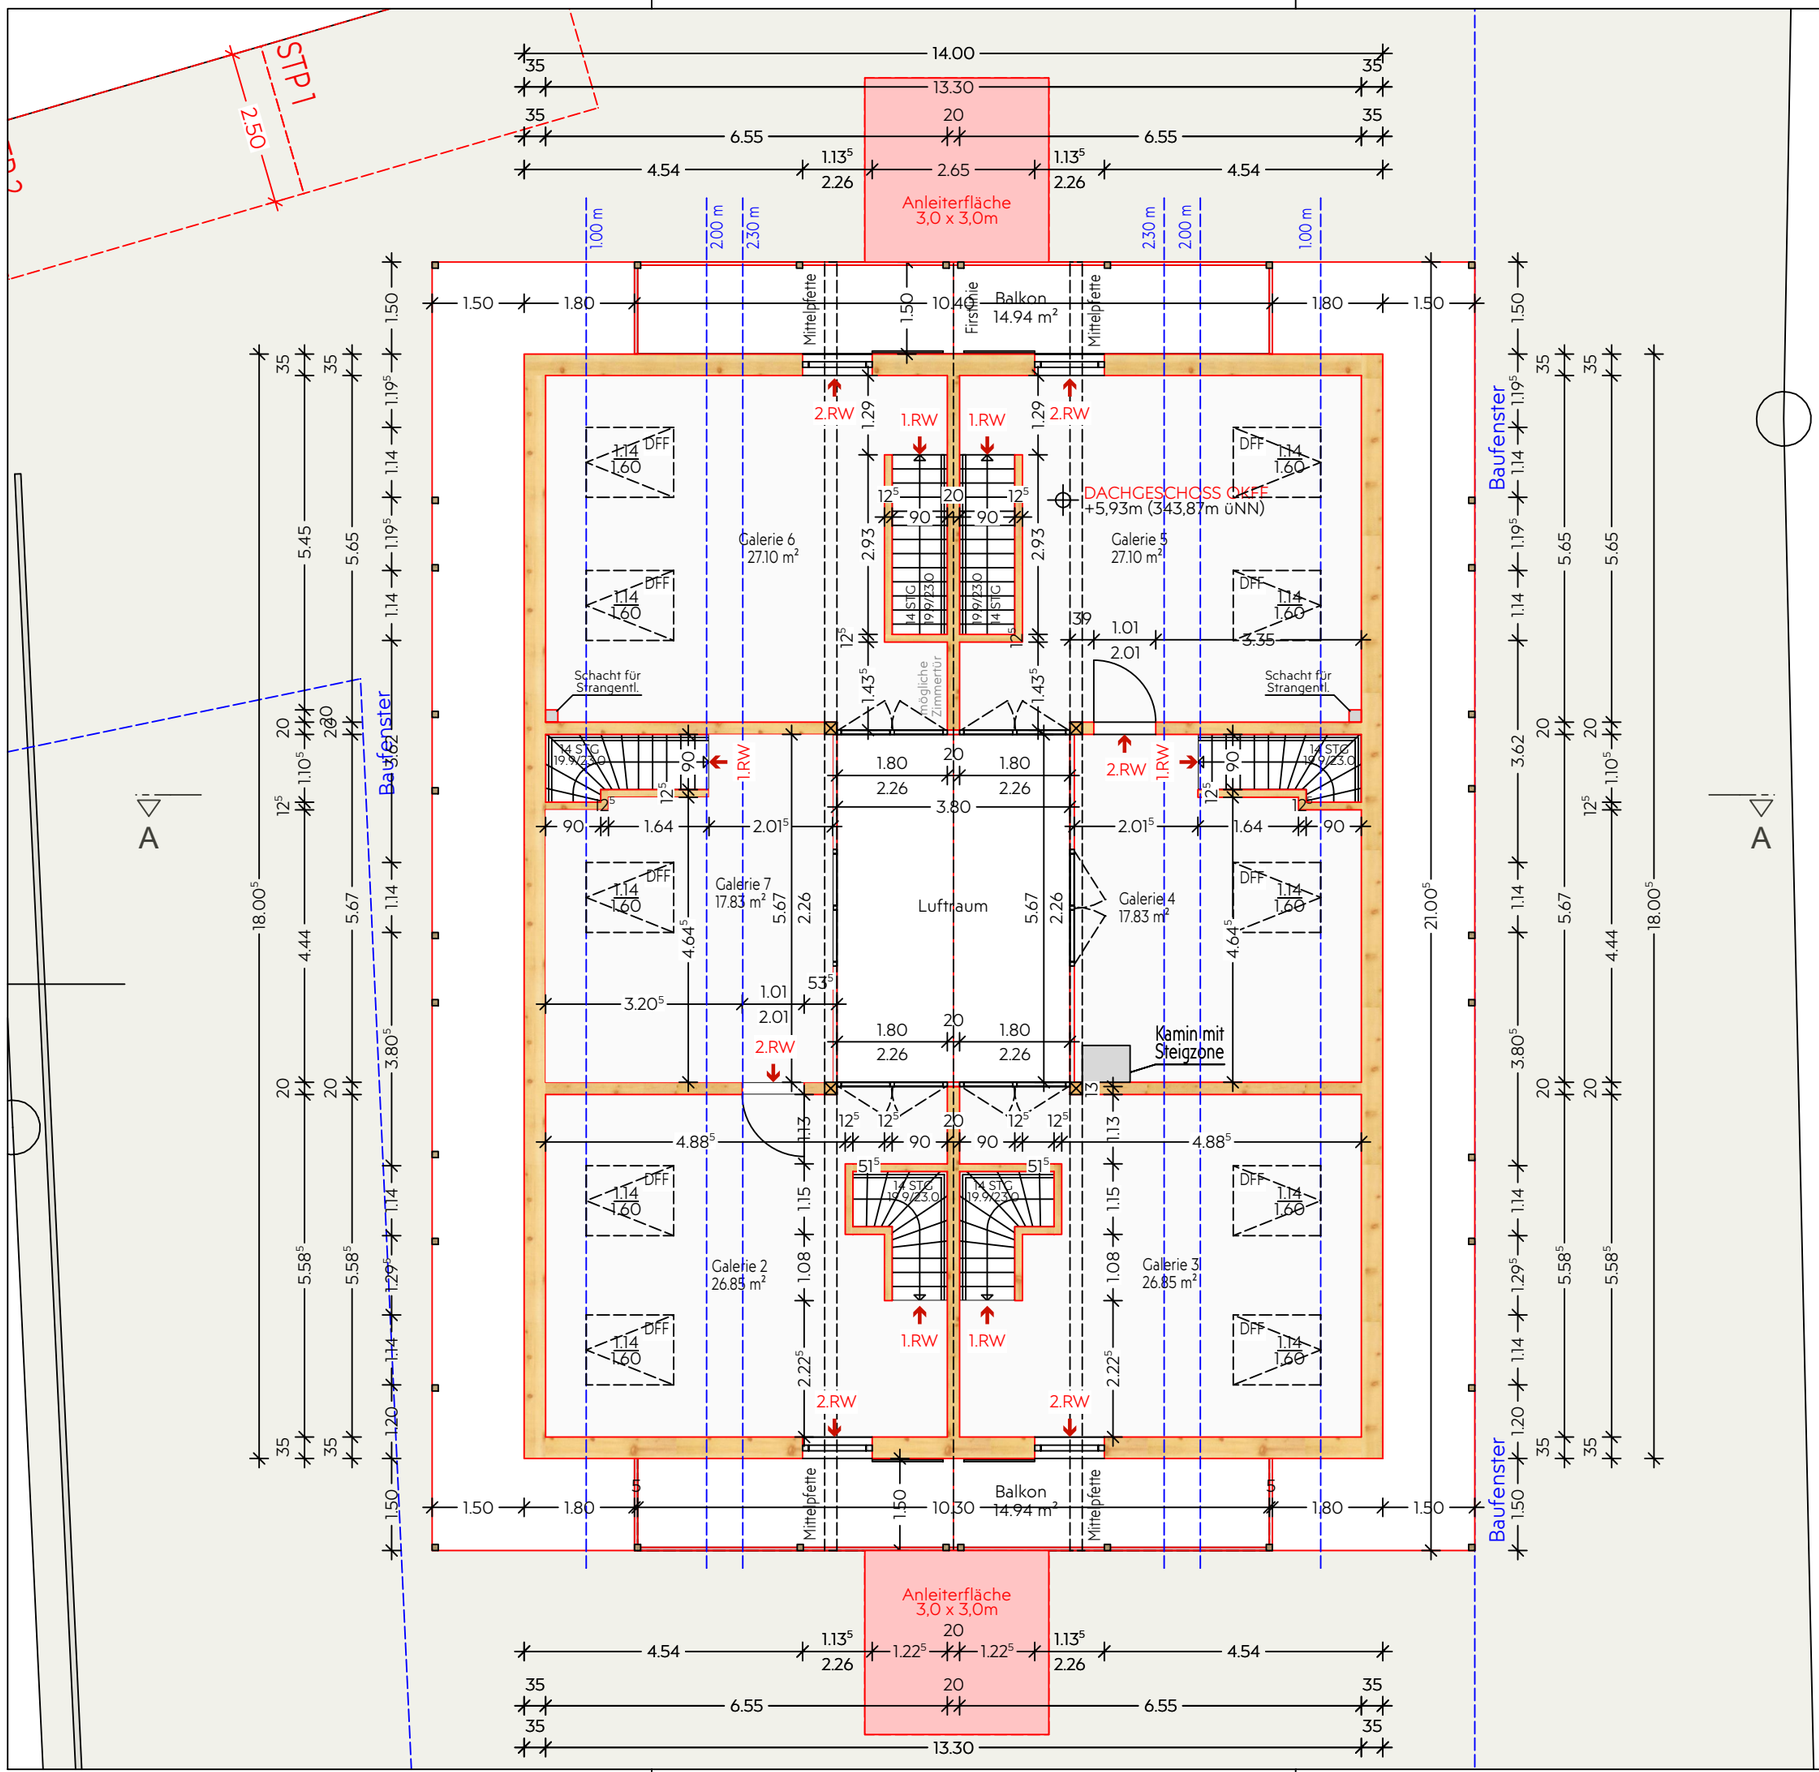


STATUS	BAUANTRAG VORABZUG BESTAND / NEUBAU / ABBRUCH
PROJEKT	Neubau eines Wohnhauses mit gemeinschaftlich nutzbaren Wohneinheiten Sonnenweg 6 79539 Lörrach
BAUHERR	Jeremy Tammik Mühlesteig 7 CH-4102 Binningen
ARCHITEKT	KURIARCHITEKTEN BDA Belchenstraße 80 79650 Schopfheim +49 7622 684 36 75 info@kuriarchitekten.de kuriarchitekten.de KURI 2 AUSSEN TRIFFT INNEN
PLAN	Grundriss - Dachgeschoss A3
DATUM	18.11.2024 · 1:100 · LK
VERFASSER	Unterschrift Bauherr · Unterschrift Architekt