


29.10.24

- 1. Zw führt über die jeweils not-
wendige Treppe ins 2. und von
dort über die vorhandenen
RW ins 3. u.

2. Zw führt zur Ankerfläche
und von dort über Rettungs-
galerie der Feuerwe-

- Zugangslokat Galerie 7 zu
2 und von 4 zu 5
2 ist sicherzustellen

- die Stellflächen 3x3m
sind gem. VWV Feuer-
wehrplan auszubilden

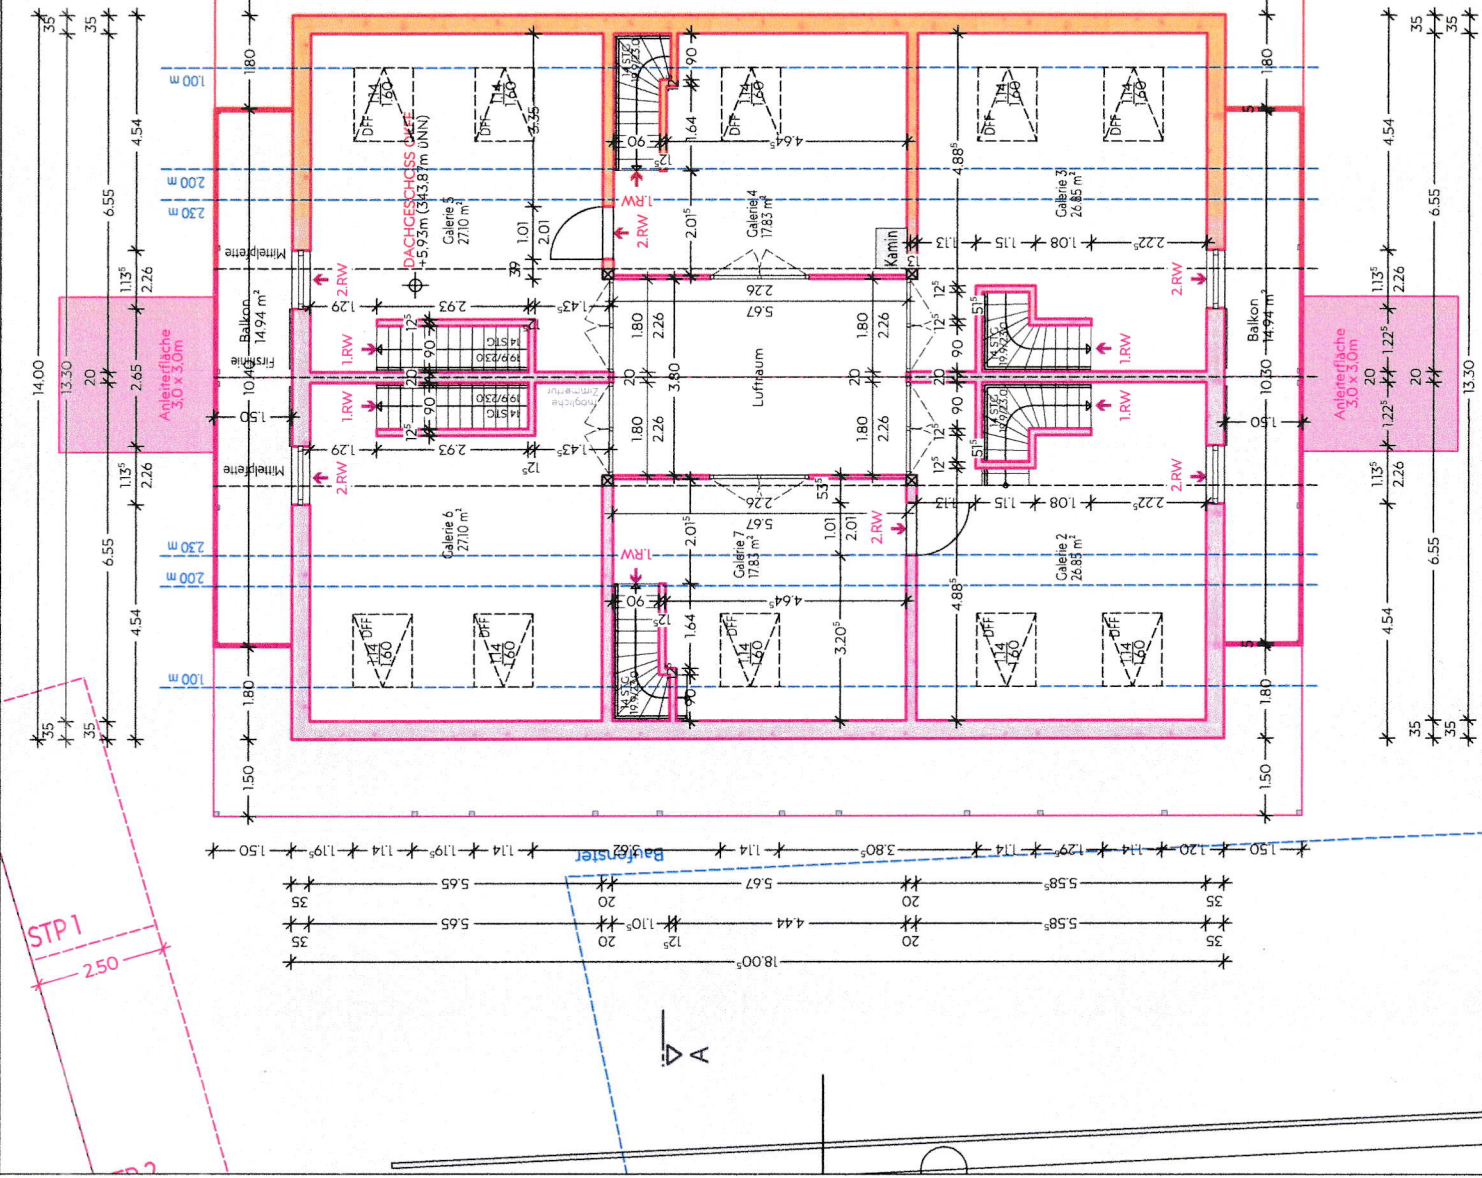

BAUANTRAG		BESTAND		ABBRUCH	
Neubau eines Wohnhauses mit gemeinschaftlich nutzbaren Wohneinheiten Sonnenweg 6 79539 Lörrach		NEUBAU		ABBRUCH	
Jeremy Tammik Mühlsteig 7 CH-4102 Birmingen		KURI 2		AUSSEIN TRIFFT INNEN	
KURIARCHITEKTEN BDA Belchenstraße 80 79650 Schopfheim +49 7622 484 36 75 info@kuriarchitekten.de kuriarchitekten.de		Grundriss - Dachgeschoss A3		LK	
PLAN		29.08.2024		1:100	
DATUM		Unterschrift Bauherr		Unterschrift Architekt	
VERFASSTER		Allplan 2024			

geprüft
Tina Jurek
Ber Gmst

H/B = 297 / 420 (0.12m²)