


N:\Binkert_Plan_GmbH\Projekte\2023-12-1 Tammik Lorrach\01_Vorbereitung\2023-12-1_Tammik Lorrach_VPH_GR_01_BP_2023-03-10.mxd

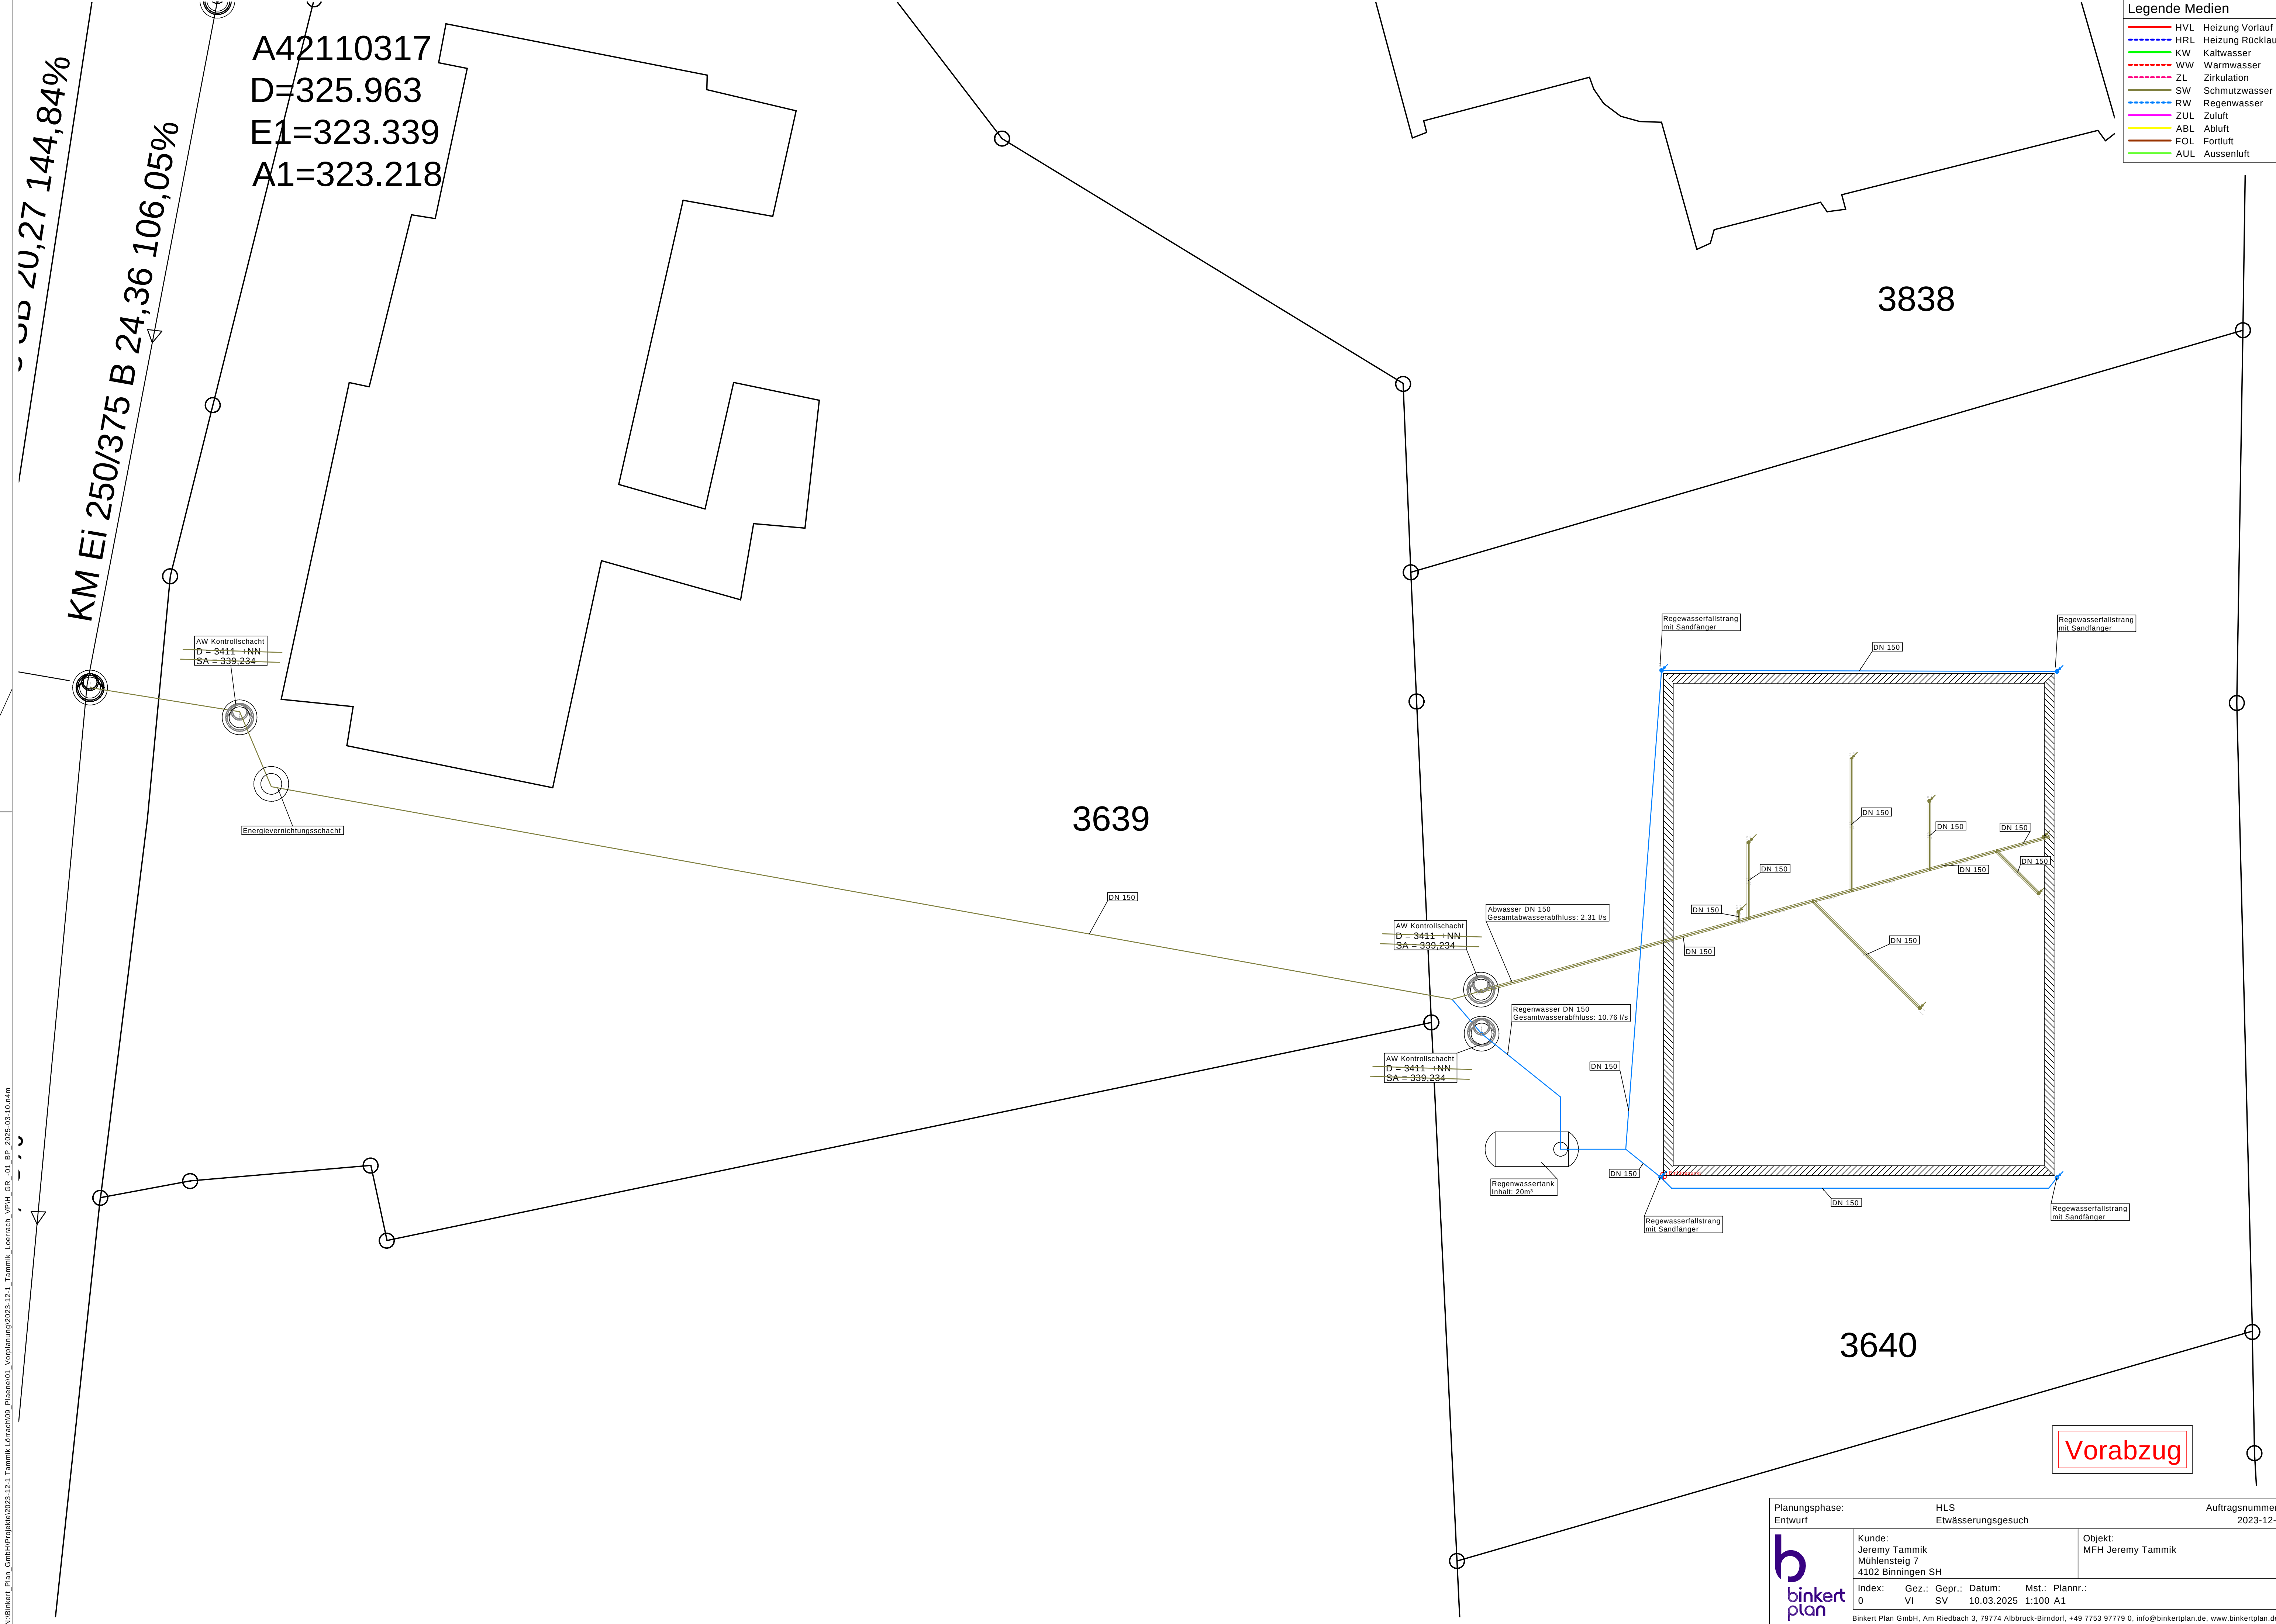

Legende Medien	
—	HVL Heizung Vorlauf
- - -	HRL Heizung Rücklauf
—	KW Kaltwasser
- - -	WW Warmwasser
- - -	ZL Zirkulation
—	SW Schmutzwasser
- - -	RW Regenwasser
—	ZUL Zuluft
—	ABL Abluft
—	FOL Fortluft
—	AUL Aussenluft

A42110317
D=325.963
E1=323.339
A1=323.218

~ 20,27 144,84%
KM Ei 250/375 B 24,36 106,05%

AW Kontrollschacht
D = 3411 +NN
SA = 339.234

Energievernichtungsschacht

3639

AW Kontrollschacht
D = 3411 +NN
SA = 339.234

Abwasser DN 150
Gesamtabwasserabfluss: 2.31 l/s

Regenwasser DN 150
Gesamtwasserabfluss: 10.76 l/s

AW Kontrollschacht
D = 3411 +NN
SA = 339.234

Regenwassertank
Inhalt: 20m³

3838

3640

Vorabzug

Planungsphase: Entwurf		HLS Etwässerungsgesuch		Auftragsnummer: 2023-12-1	
	Kunde: Jeremy Tammik Mühlensteig 7 4102 Binningen SH			Objekt: MFH Jeremy Tammik	
	Index: 0	Gez.: SV	Gepr.: 10.03.2025	Mst.: 1:100	Plannr.: A1
Binkert Plan GmbH, Am Riedbach 3, 79774 Albrück-Birndorf, +49 7753 97779 0, info@binkertplan.de, www.binkertplan.de					