


KM Ei 250/375 B 24,36 106,05%

Huenerbergweg

42110318 Kanalschacht
D = 323.133 m
E1 = 320.649 m
A1 = 320.595 m

S05 Übergabeschacht
DN1000
D 326.004 m
S ??? m

S04 Energieumwandlungsschacht
DN1000
D 325.950 m
S ??? m

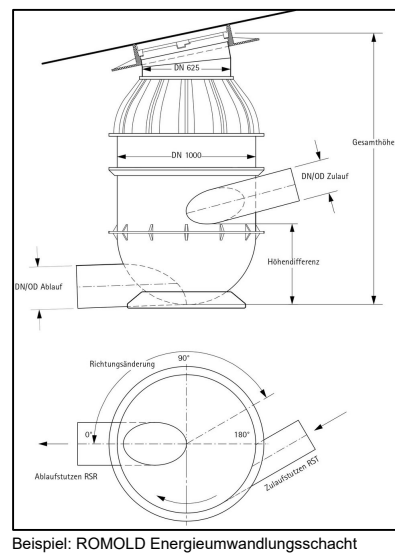

Beispiel: ROMOLD Energieumwandlungsschacht


18,6 %
DN100

3639

Schmutzwasserabfluss
mit Abflusskennzahl 0,5 = 2,31 l/s

Regenwasserabfluss
nach Drosselschacht = 5,50 l/s


S03 Absturzschaft
DN1000
D 337.940 m
S 333.443 m

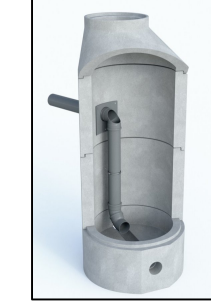

Beispiel: FUNKE I.A. innenliegender Absturz

S04 Kontrollschacht
DN1000
D 334.243 m
S 333.343 m

S02 Drosselschacht
DN600
D 335.558 m
S 333.683 m


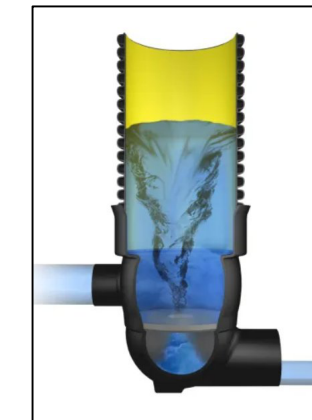


Beispiel: FRANKISCHE Rigo Limit V

3838

3640

Kontur Laubengang
und Dachüberstand

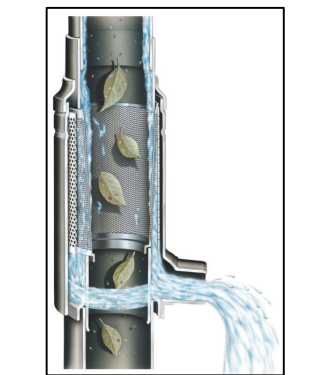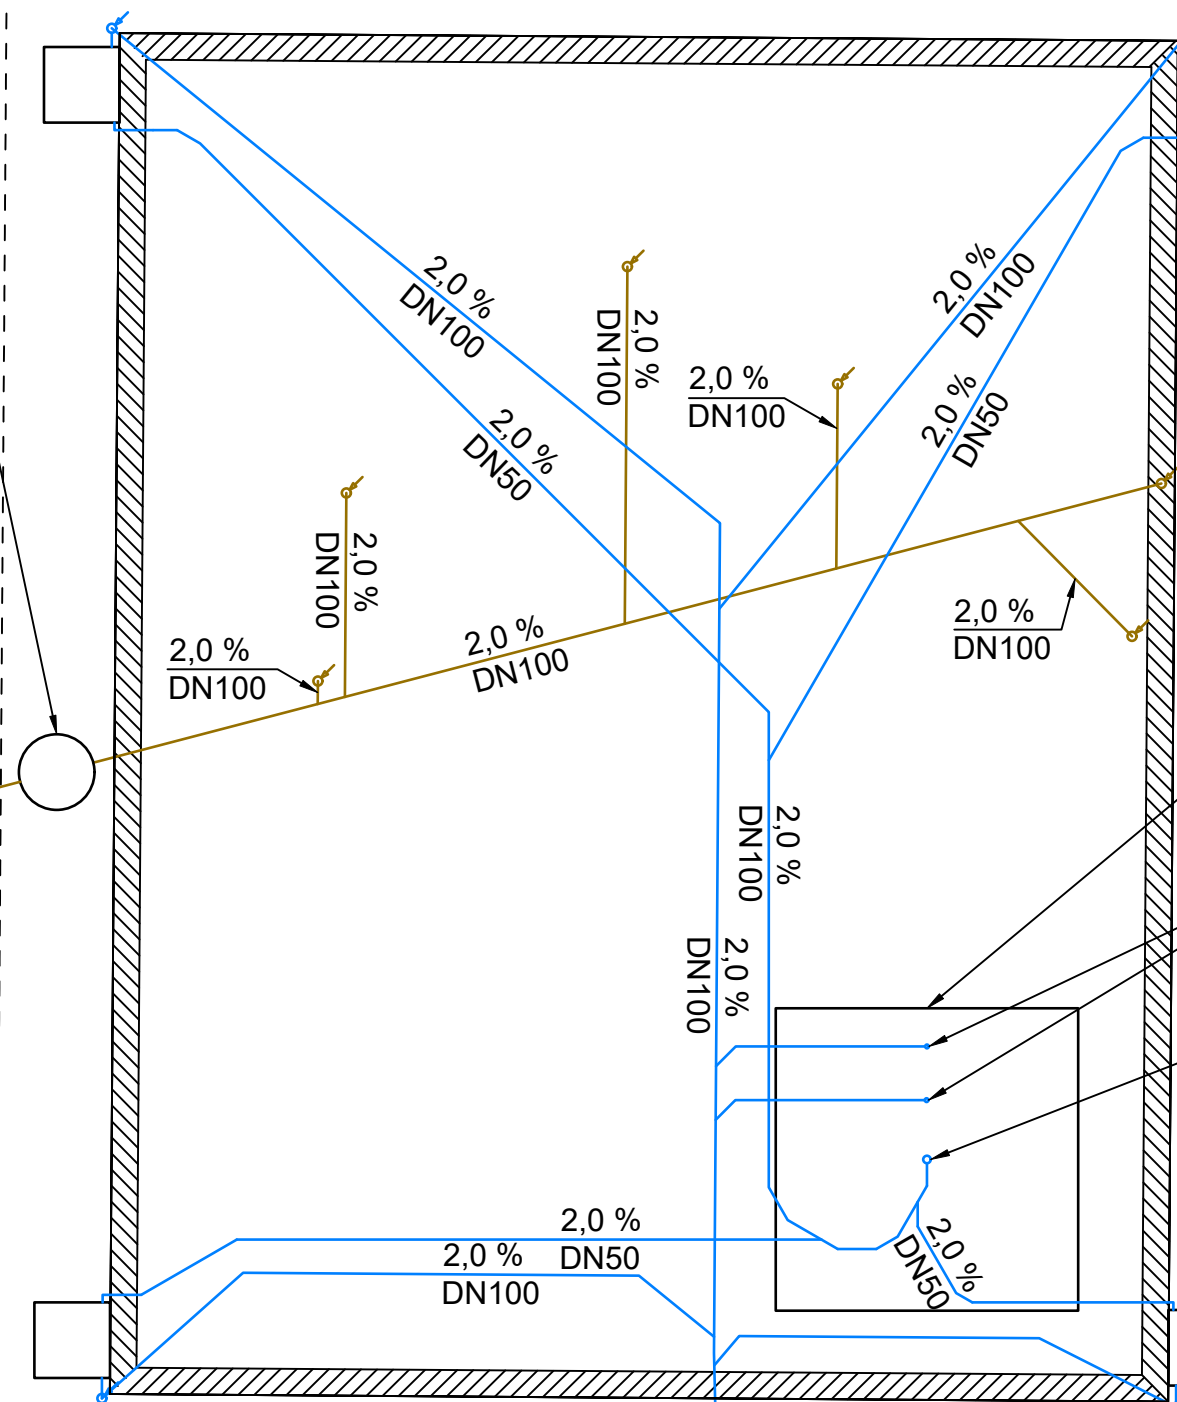

Beispiel: WSV Filtersammel FS

Fallrohrfilter
für mind. 90 qm
Dachfläche

Regenwassertank
zur oberirdischen
Aufstellung

Regenwasserüberlauf
DN50

Zisterne

Zisternenüberlauf
DN50 x2

Zisterneneinlauf
DN100

S01 Filterschacht
DN350
D 337.940 m
S 336.815 m



Beispiel: PREMIER TECH Rewatec Vorflut Mau-Pipe

Retentionsmulde
4,62 cbm
OK 335.558 m
S 335.158 m

Regenwasserabfluss
mit $r(5,2) = 10,92$ l/s

Einlaufbereich
OK 335.558 m
UK 335.158 m

3641

Sonnenweg

Legende

— RW Regenwasser
— SW Schmutzwasser / Mischwasser

Index			Änderungen		Datum	Name
Projekt:			Am Waldrain Sonnenweg 6 79539 Lörrach			
Bauherr:			Jeremy Tammik Mühlesteg 7 CH-4102 Binningen			
Architektur:			Dipl.-Ing. (FH) Thomas Kuri Schwarzwaldstraße 22 79650 Schopfheim			
Planverfasser:			Markus (Marek) Pasterny - Beratender Ingenieur Pannierstraße 21 12047 Berlin			
Projekt-Nr.:		Datum:	Maßstab:	Blattgröße:		
25-007		14.05.2025	1:100	A1 (841x594) mm		
Planbezeichnung:					Projektphase:	
Entwässerungsplan					LP 4	
Plan-Nr.: 007-4-EWP-551-100--						