


KM Ei 250/375 B 24,36 106,05%

Huenerbergweg

42110318 Kanalschacht
D = 323.133 m
E1 = 320.649 m
A1 = 320.595 m

S06 Übergabeschacht
DN1000
D 326.004 m
S 324.034 m

S05 Energieumwandlungsschacht
DN1000
D 325.950 m
S 324.091 m

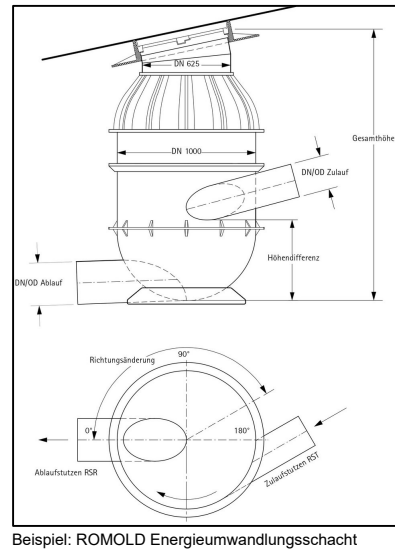

Beispiel: ROMOLD Energieumwandlungsschacht


20,0 %
DN100

3639

Schmutzwasserabfluss
mit Abflusskennzahl 0,5 = 2,36 l/s

Regenwasserabfluss
nach Drosselschacht = 5,50 l/s

S03 Absturzschaft
DN1000
D 337.940 m
S 333.443 m

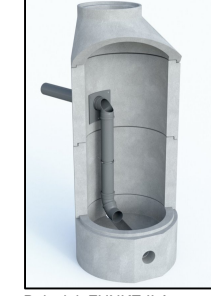


Beispiel: FUNKE I.A. innenliegender Absturz

S04 Kontrollschacht
DN1000
D 334.243 m
S 333.343 m

2,0 %
DN100

S02 Drosselschacht
DN600
D 335.558 m
S 333.683 m

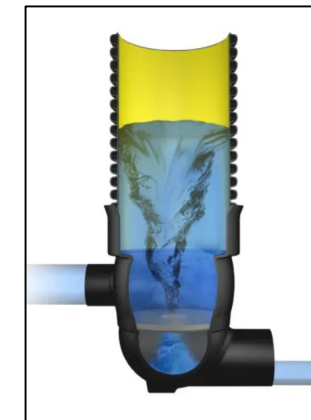

Beispiel: FRANKISCHE Rigo Limit V

Retentionsmulde
4,31 cbm
OK 335.558 m
S 335.258 m

Regenwasserabfluss
mit $r(5,2) = 12,14$ l/s



Beispiel: PREMIER TECH Rewatec Vorflut Mau Plus

Einlaufbereich
OK 335.558 m
UK 335.258 m

Retentionsmulde
4,31 cbm
OK 335.558 m
S 335.258 m

3640



Beispiel: WSV Filtersammel FS

Fallrohrfilter
für mind. 90 qm
Dachfläche

Regenwassertank
zur oberirdischen
Aufstellung


Regenwasserüberlauf
DN50

Zisterne

Zisternenüberlauf
DN50 x2


Zisterneneinlauf
DN100

S01 Filterschacht
DN350
D 337.940 m
S 336.655 m

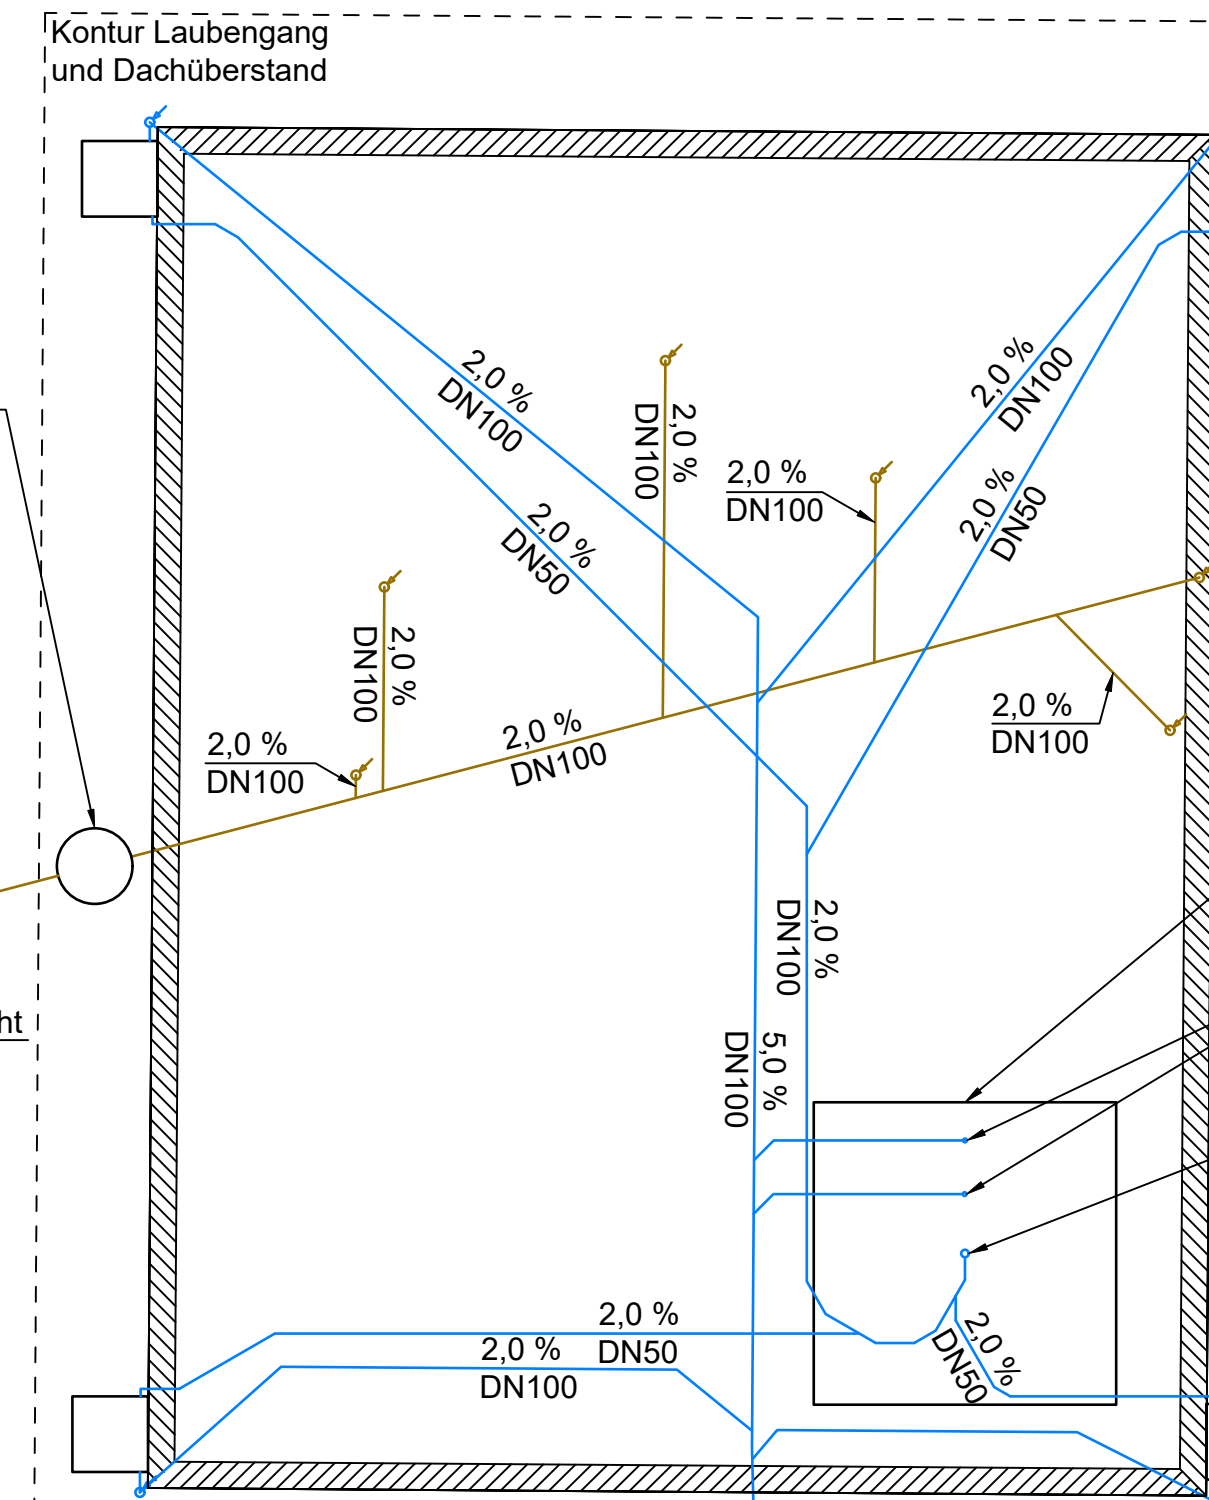

3641

Schnitt Retentionsmulde
und Drosselschacht

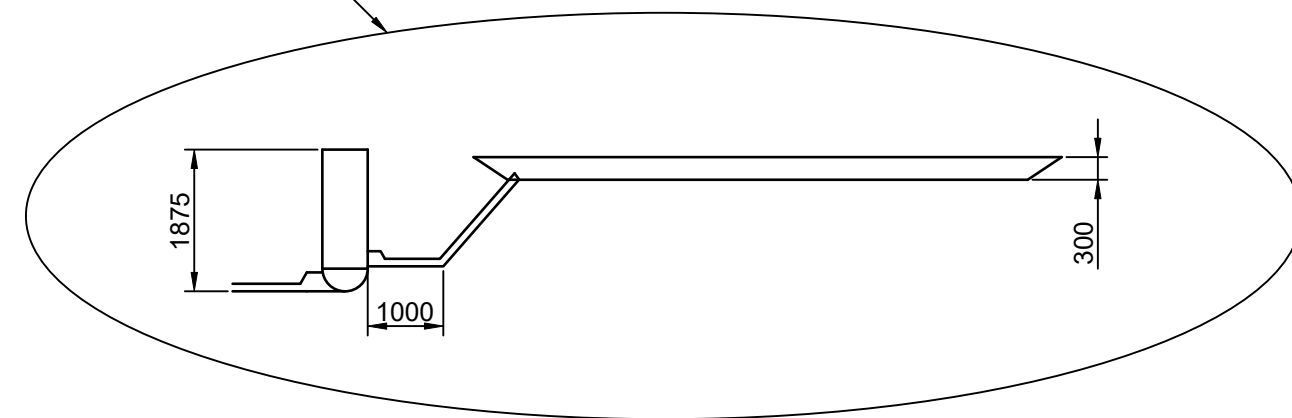

Legende

— RW Regenwasser
— SW Schmutzwasser / Mischwasser

Index Änderungen				Datum	Name
Projekt: Am Waldrain Sonnenweg 6 79539 Lörrach					
Bauherr: Jeremy Tammik Mühlesteg 7 CH-4102 Blinningen					
Architektur: Dipl.-Ing. (FH) Thomas Kuri Schwarzwaldstraße 22 79650 Schopfheim					
Planverfasser: Markus (Marek) Pasterny - Beratender Ingenieur Pannierstraße 21 12047 Berlin					
Projekt-Nr.: 25-007	Datum: 02.06.2025	Maßstab: 1:100	Blattgröße: A1 (841x594) mm		
Planbezeichnung: Entwässerungsplan					Projektphase: LP 4
Plan-Nr.: 007-4-EWP-551-100--					