


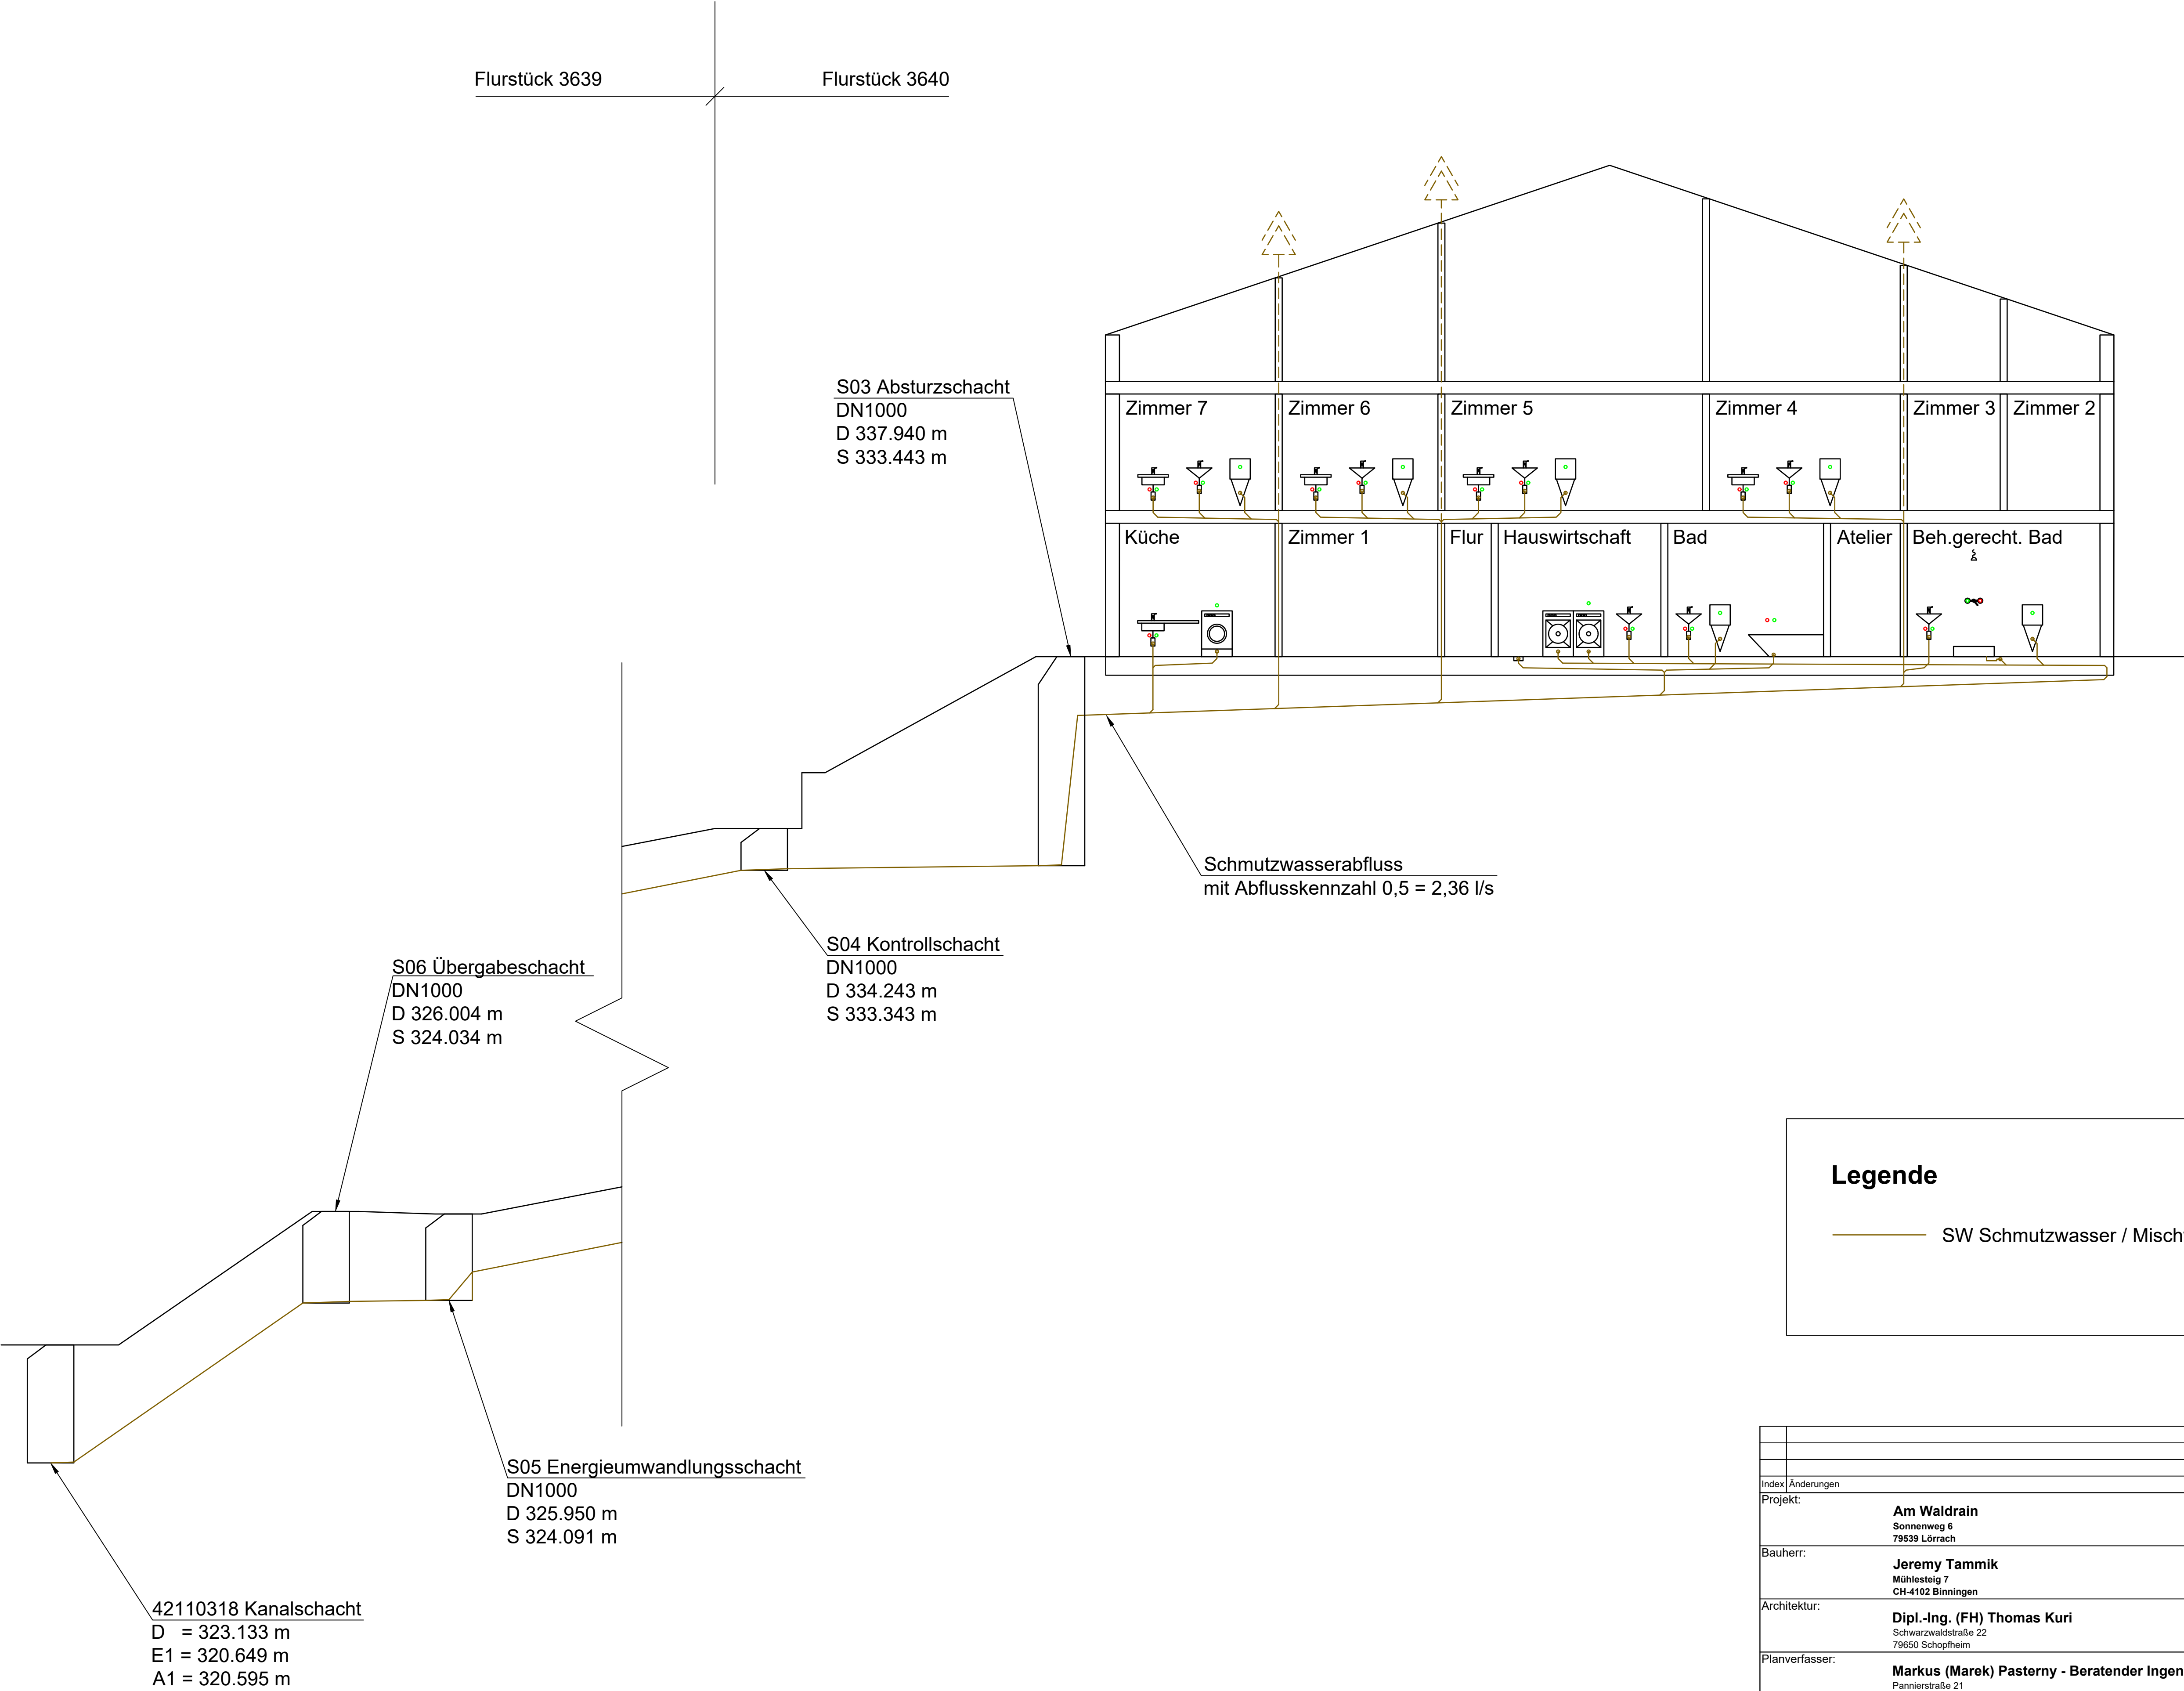

Index	Änderungen			Datum Name
Projekt: Am Waldrain Sonnenweg 6 79539 Lörrach				
Bauherr: Jeremy Tammik Mühlesteg 7 CH-4102 Blinningen				
Architektur: Dipl.-Ing. (FH) Thomas Kuri Schwarzwaldstraße 22 79650 Schopfheim				
Planverfasser: Markus (Marek) Pasterny - Beratender Ingenieur Pannierstraße 21 12047 Berlin				
Projekt-Nr.: 25-007	Datum: 02.06.2025	Maßstab: ohne	Blattgröße: A1 (841x594) mm	
Planbezeichnung: Strangschema Entwässerung			Projektphase: LP 4	
Plan-Nr.: 007-4-SSE-551-----				