


N:\Binkert_Plan_GmbH\Projekte\2023-12-1 Tamnik Lörach\09_Plaena01_Vorplanung\2023-12-1_Tamnik_Loerrach_VP\Strangschema Sanitär 2024-08-01.n4d

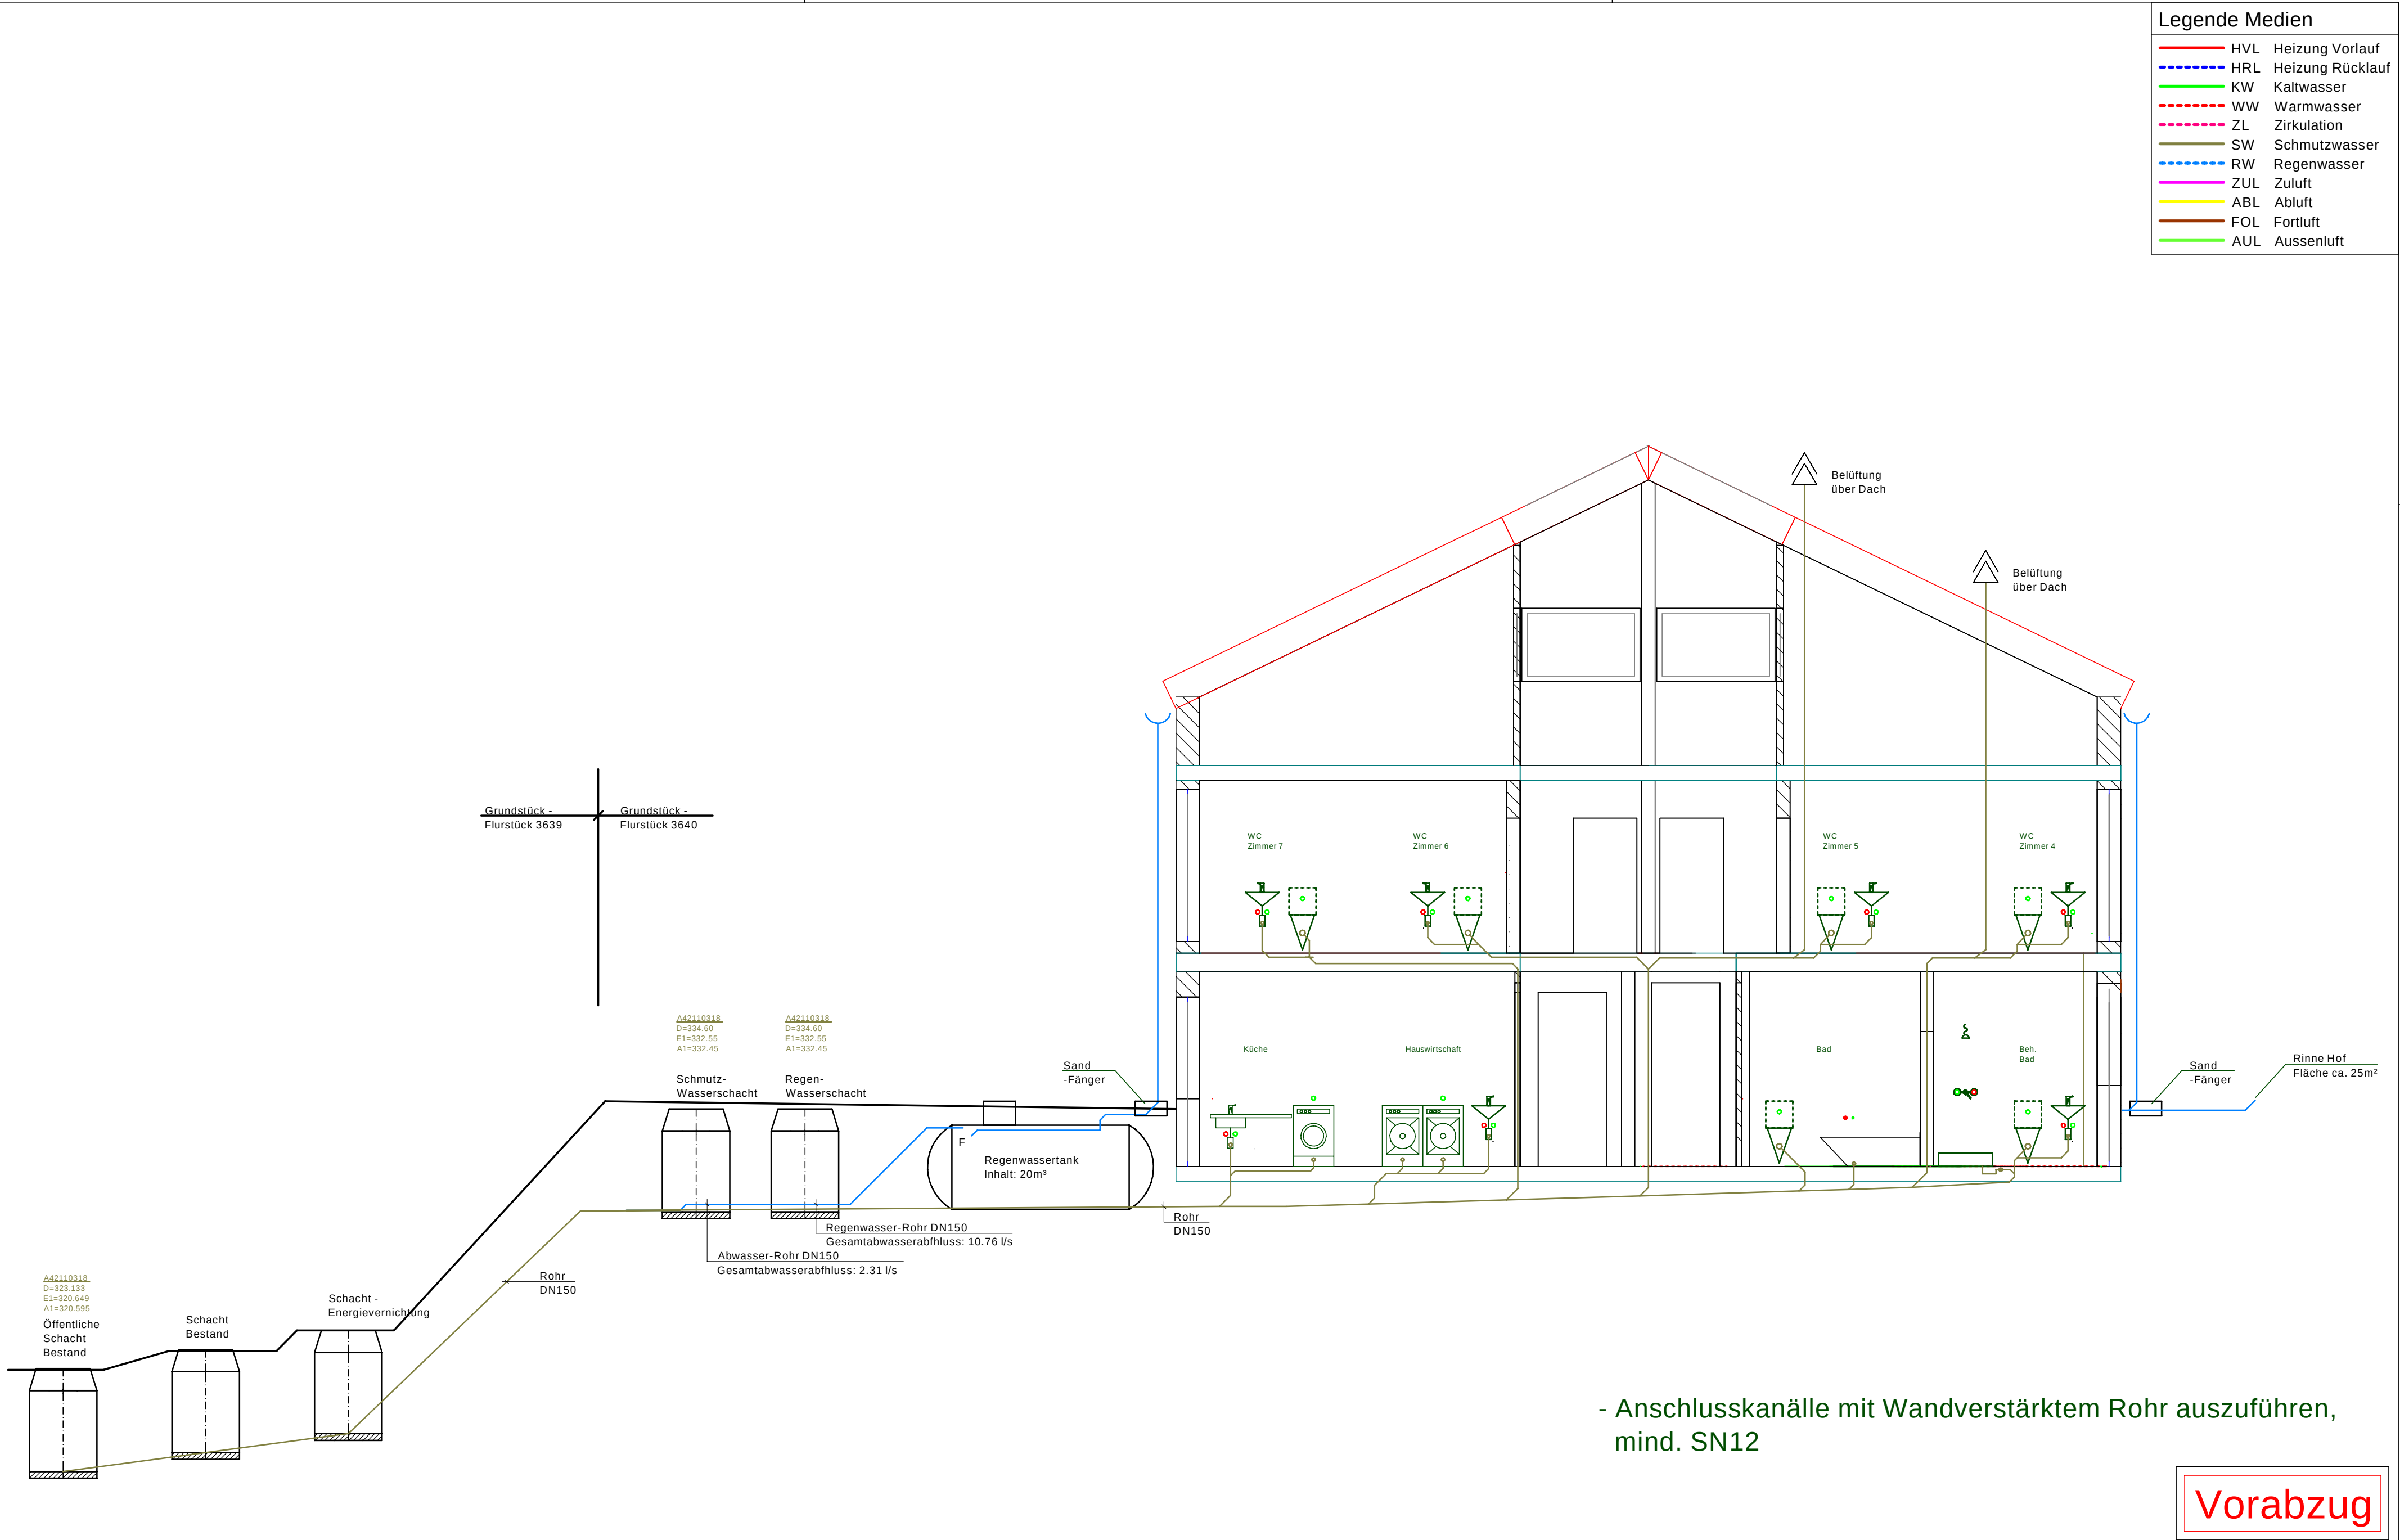

Planungsphase: Entwurf		HLS Strangschema Abwasser		Auftragsnummer: 2023-12-1	
	Kunde: Jeremy Tammik Mühlensteig 7 4102 Binningen CH			Objekt: MFH Jeremy Tammik	
	Index: 0	Gez.: CS	Gepr.: VI	Datum: 10.03.2025	Mst.: 1:63 Plannr.: A2
Binkert Plan GmbH, Am Riedbach 3, 79774 Albbruck-Birndorf, +49 7753 97779 0, info@binkertplan.de, www.binkertplan.de					